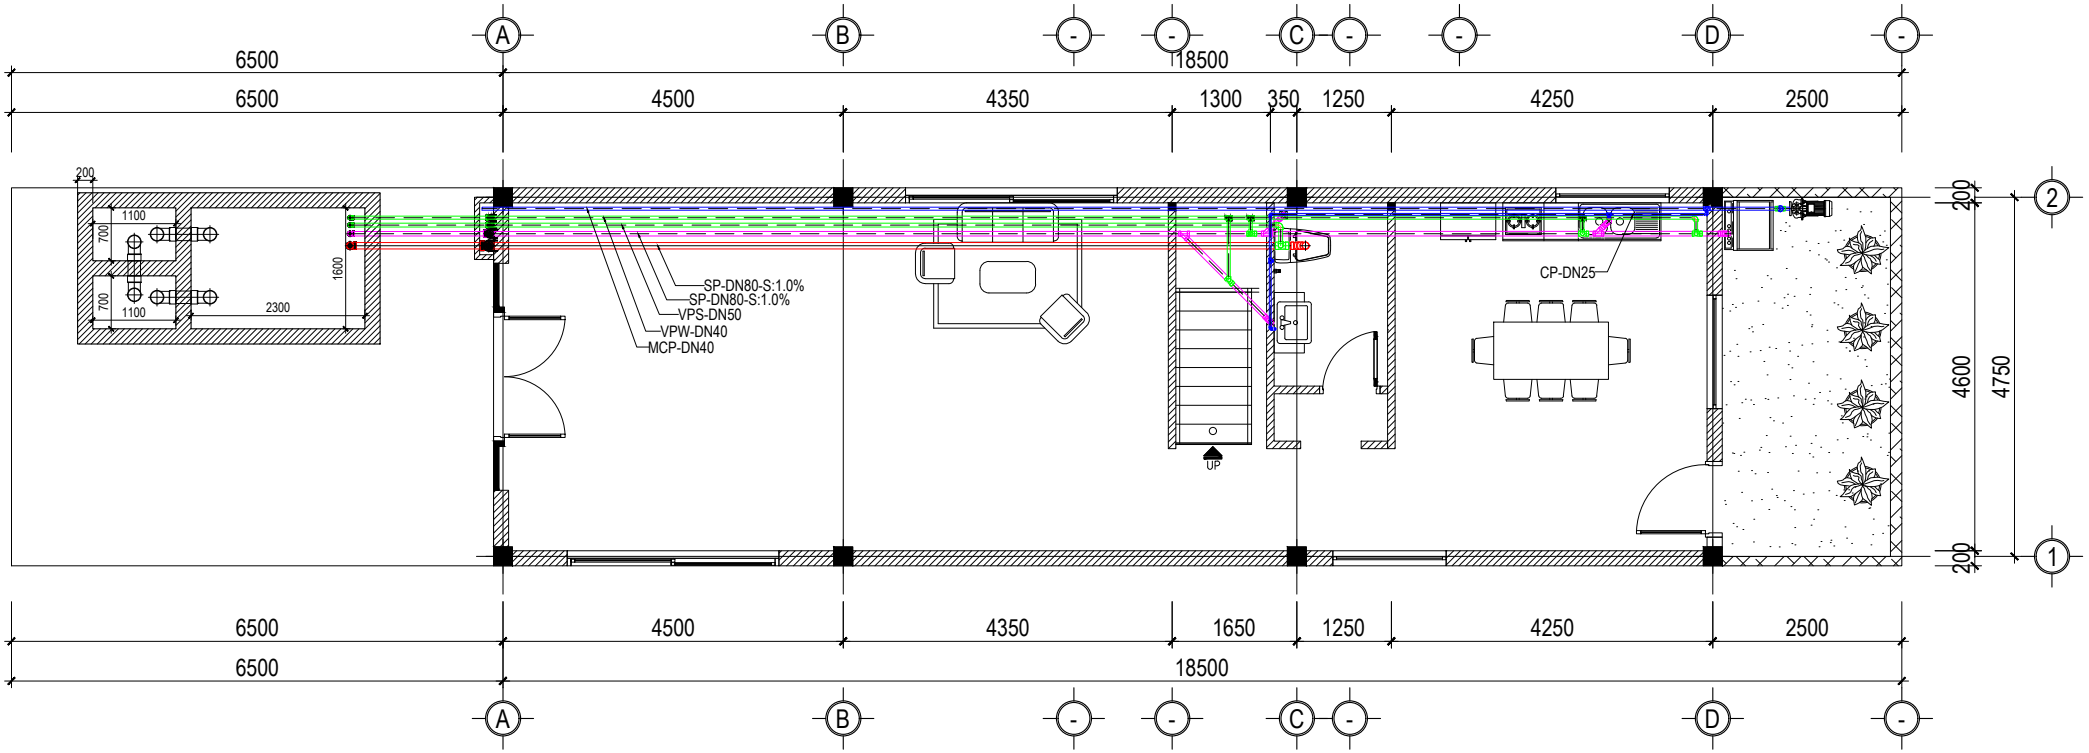

GROUND FLOOR

SCALE : 1/100

GROUND FLOOR		
SP	3"	80mm
WP	2"	50mm
VSP	2"	50mm
VWP	1.5"	40mm
CP	1.5"	25mm

Course: Installation and Sanatary Lecturer: MAY Raksmey	Student: CHUCH Manet ID: e20220847	Plumbing Plan

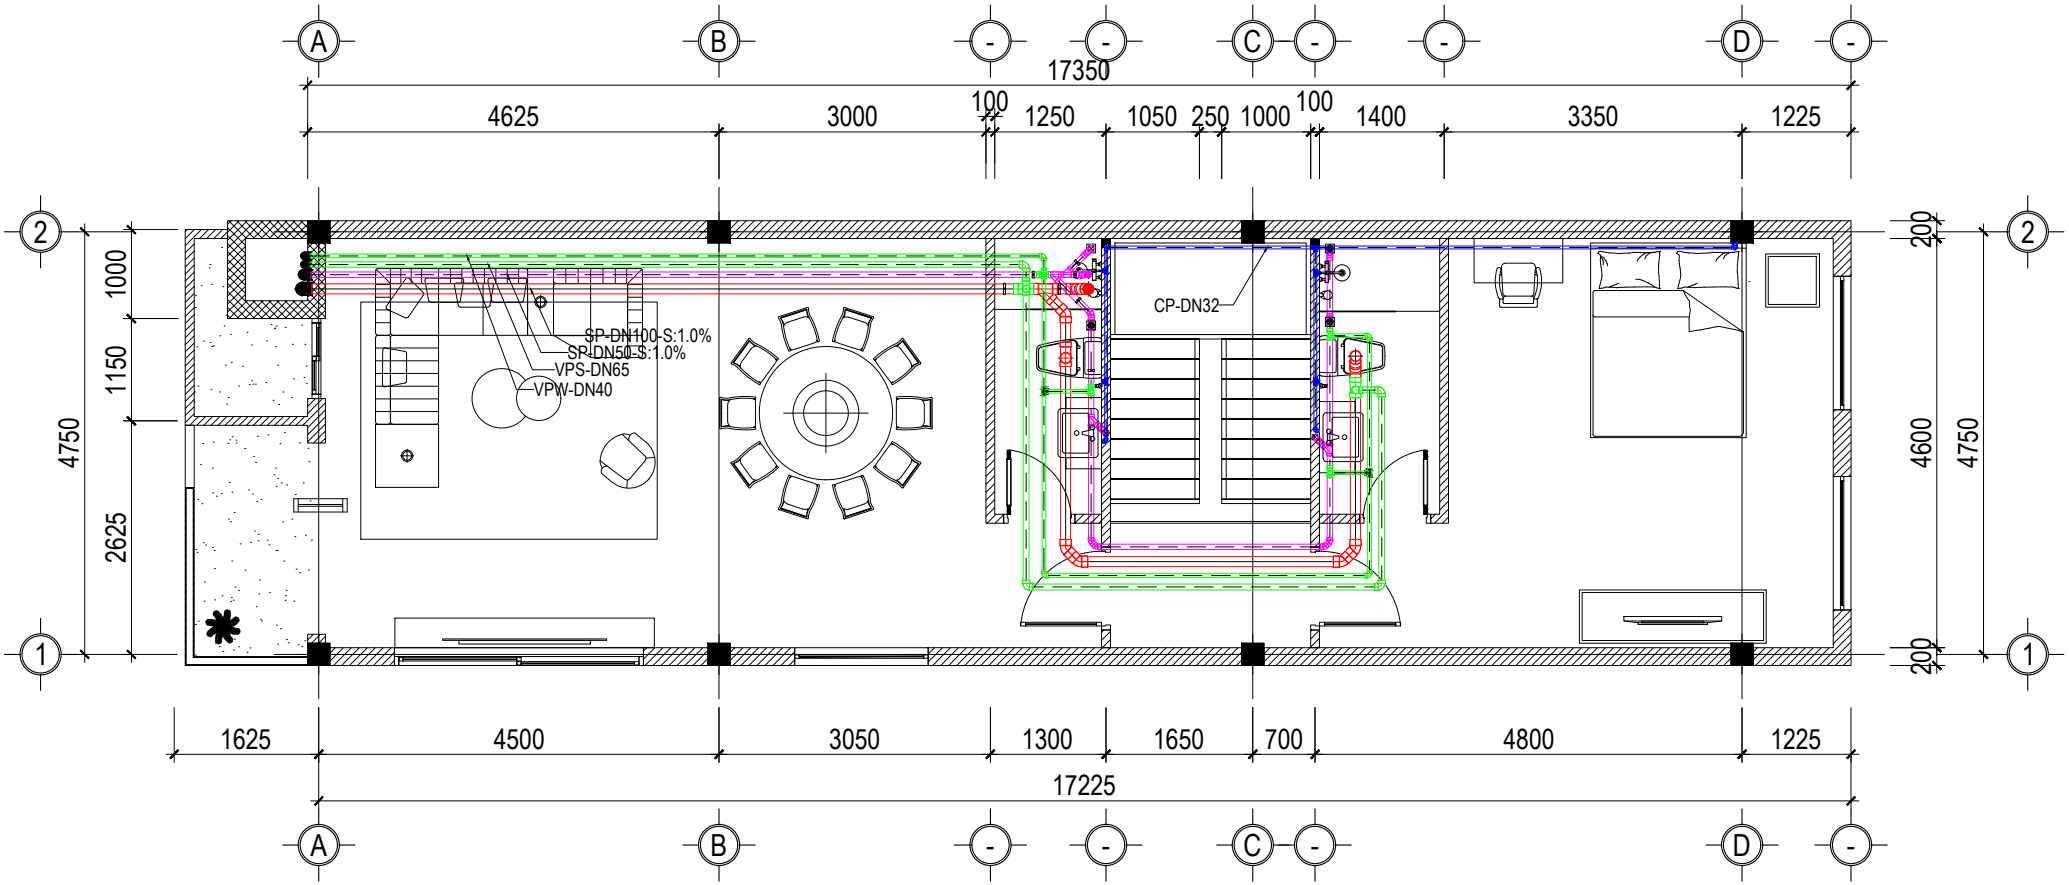

FIRST FLOOR

SCALE : 1/85

1ST FLOOR		
SP	4"	100mm
WP	2"	50mm
VSP	2.5"	65mm
VWP	1.5"	40mm
CP	1.5"	32mm

Course: Installation and Sanatary Lecturer: MAY Raksmey	Student: CHUCH Manet ID: e20220847	Plumbing Plan

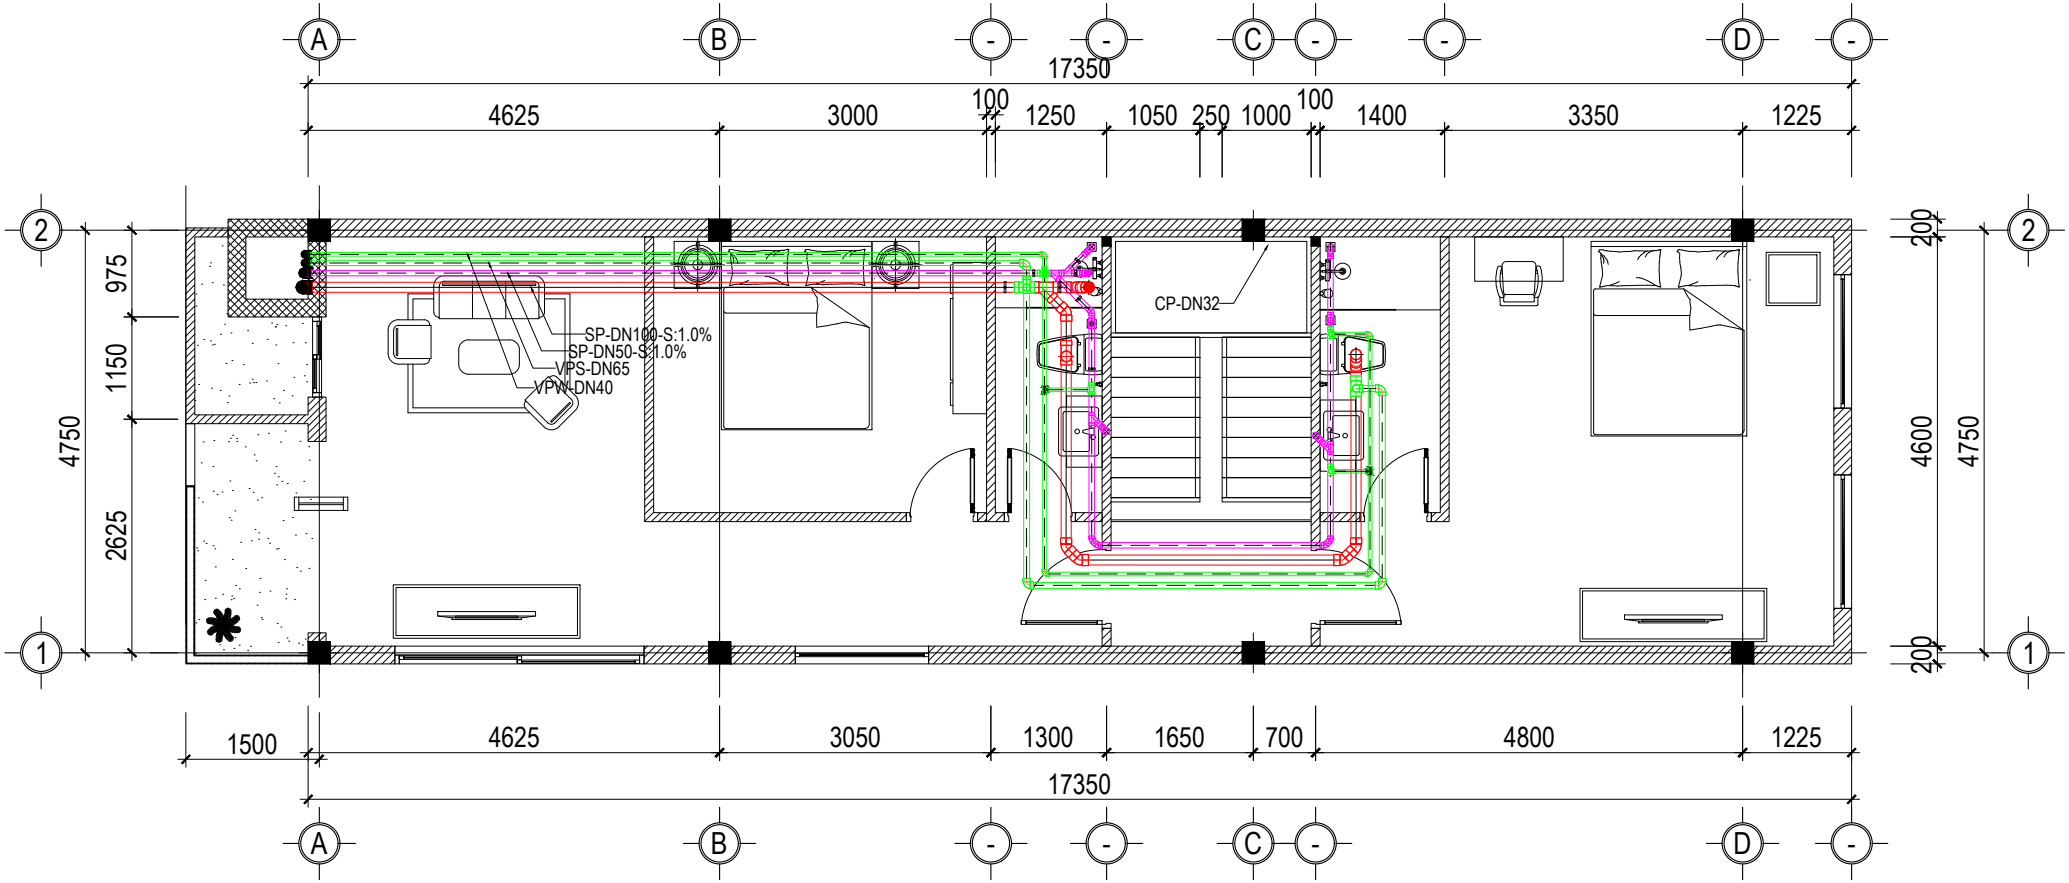

SECOND FLOOR

SCALE : 1/85

2ND FLOOR		
SP	4"	100mm
WP	2"	50mm
VSP	2.5"	65mm
VWP	1.5"	40mm
CP	1.5"	32mm

Course: Installation and Sanatary Lecturer: MAY Raksmey	Student: CHUCH Manet ID: e20220847	Plumbing Plan

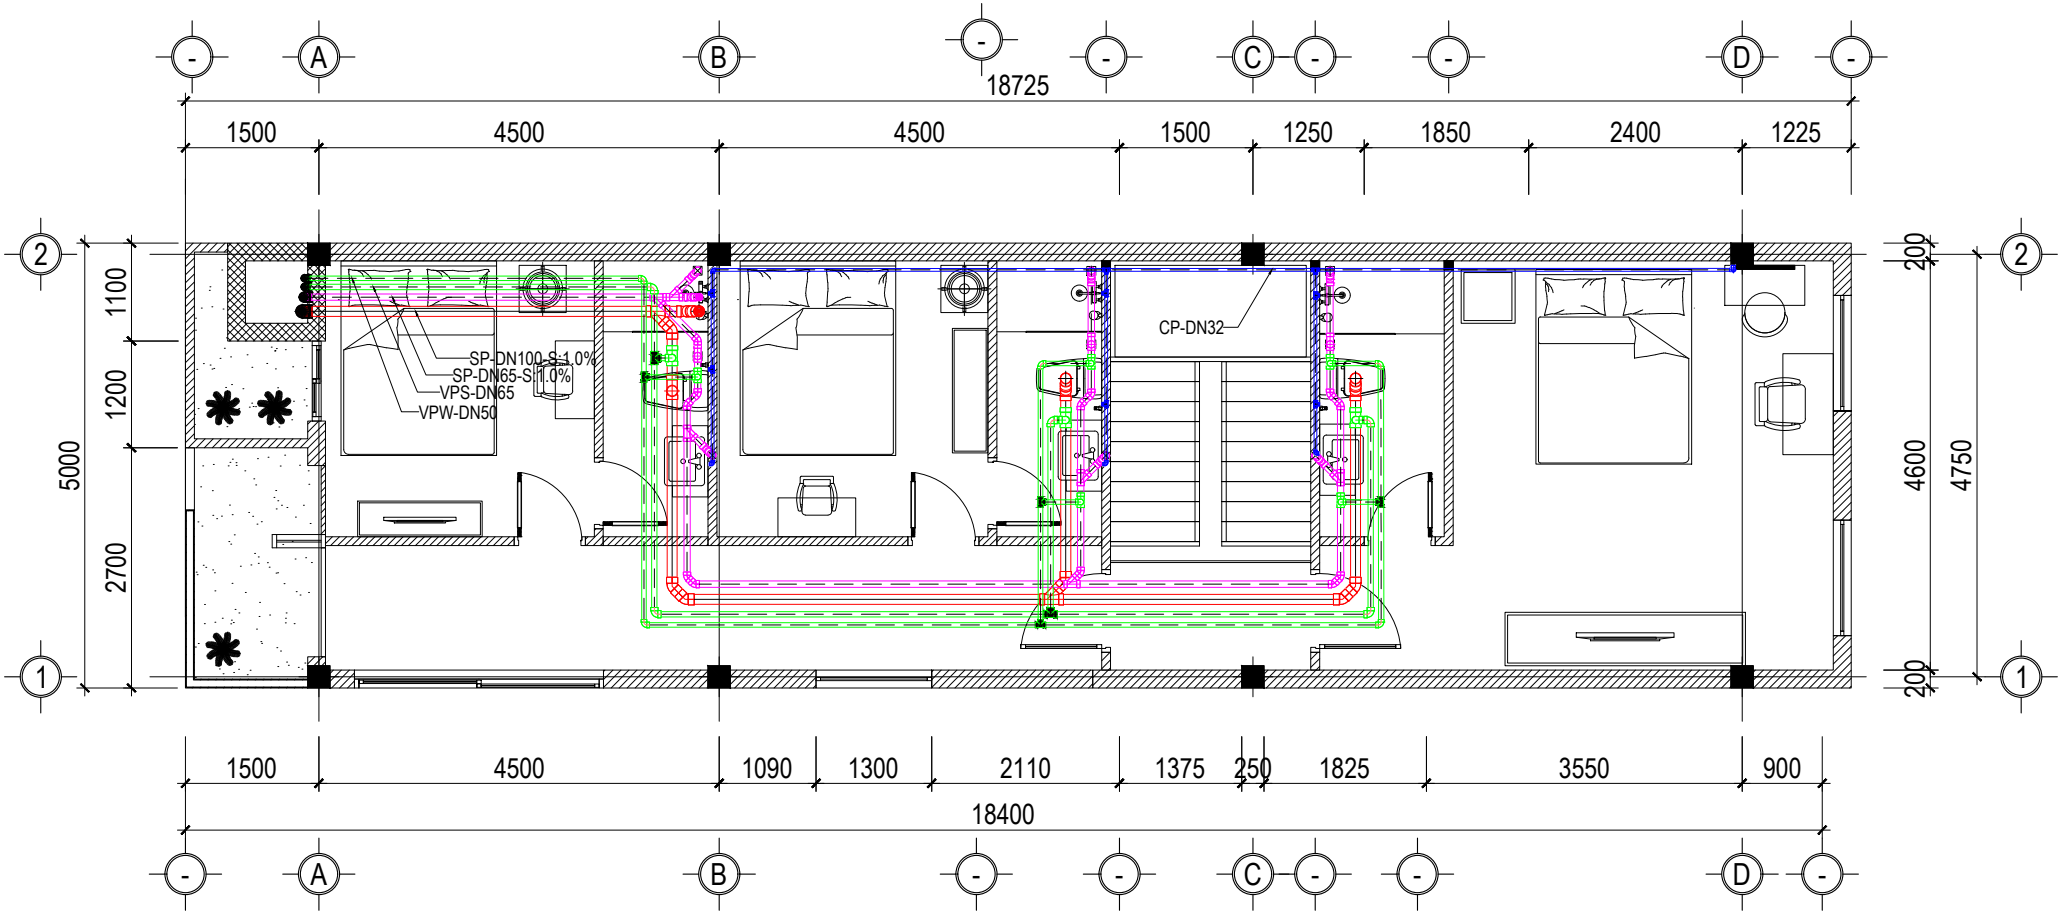

THIRD FLOOR

SCALE : 1/85

3RD FLOOR		
SP	4"	100mm
WP	2.5"	65mm
VSP	2.5"	65mm
VWP	2"	50mm
CP	1.5"	32mm

Course: Installation and Sanatary Lecturer: MAY Raksmey	Student: CHUCH Manet ID: e20220847	Plumbing Plan

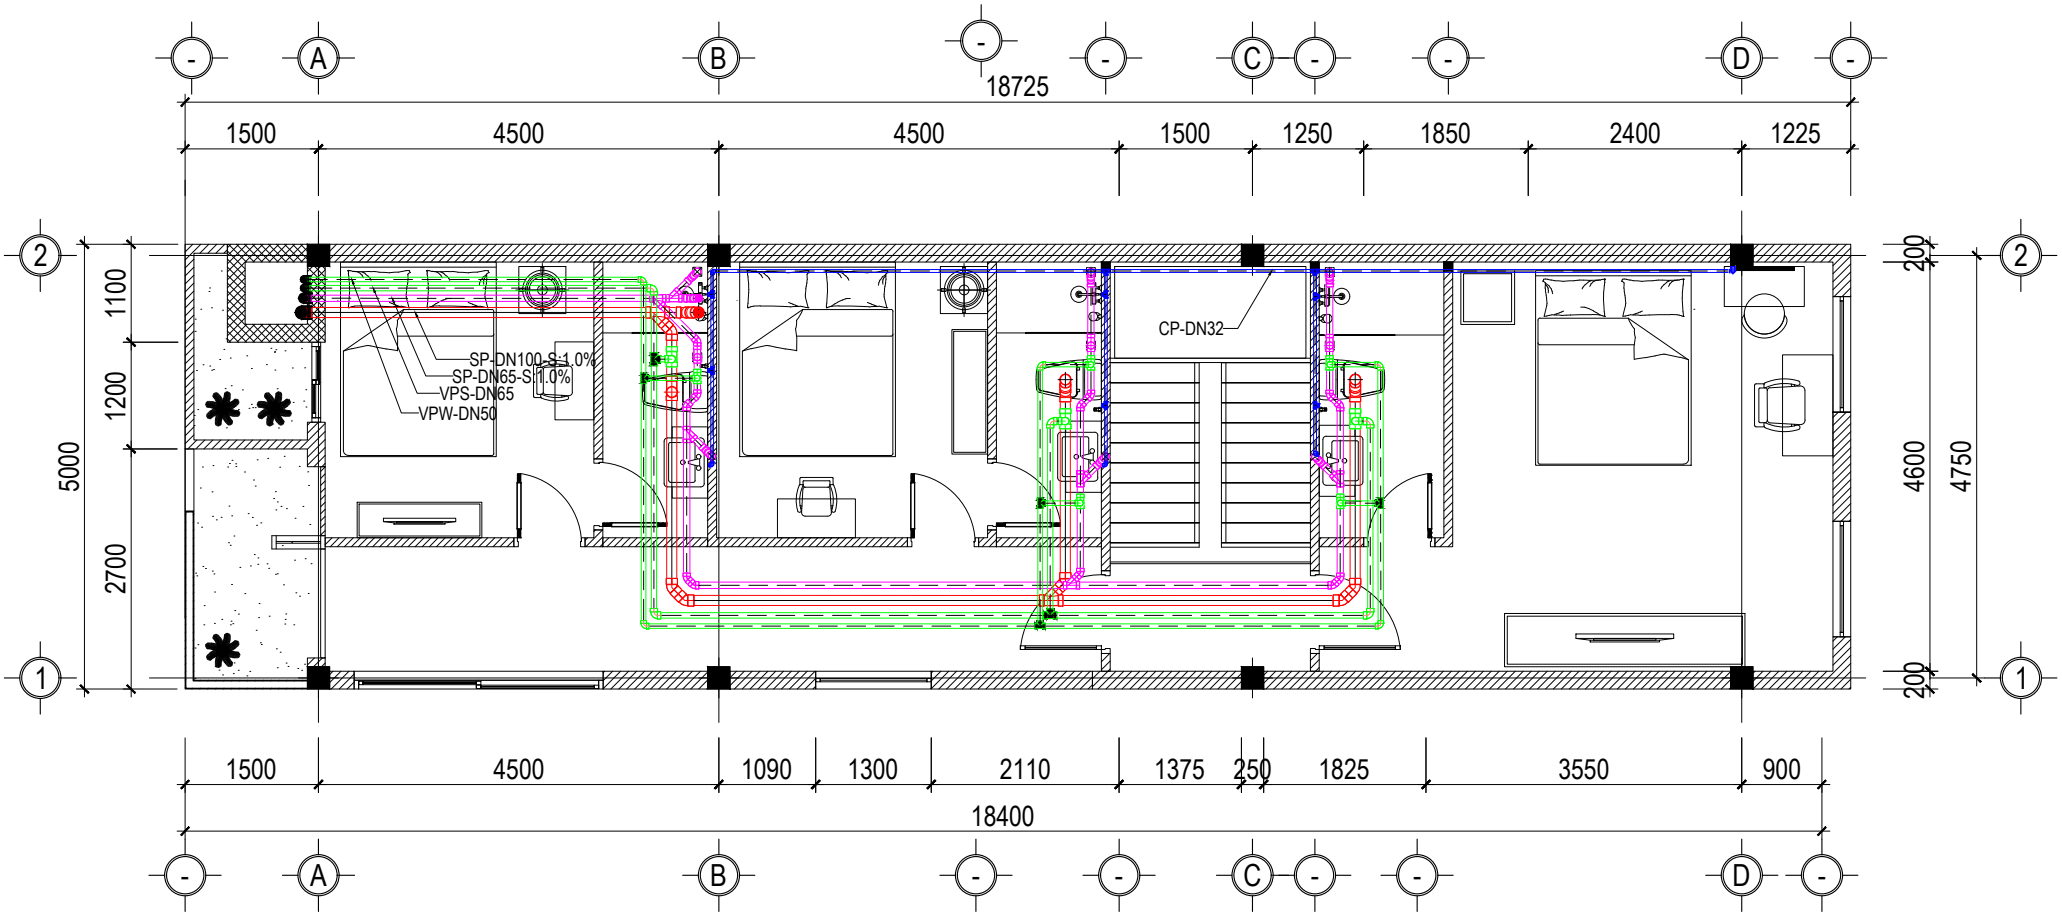

FOURTH FLOOR

SCALE : 1/85

3RD FLOOR		
SP	4"	100mm
WP	2.5"	65mm
VSP	2.5"	65mm
VWP	2"	50mm
CP	1.5"	32mm

Course: Installation and Sanatary Lecturer: MAY Raksmey	Student: CHUCH Manet ID: e20220847	Plumbing Plan

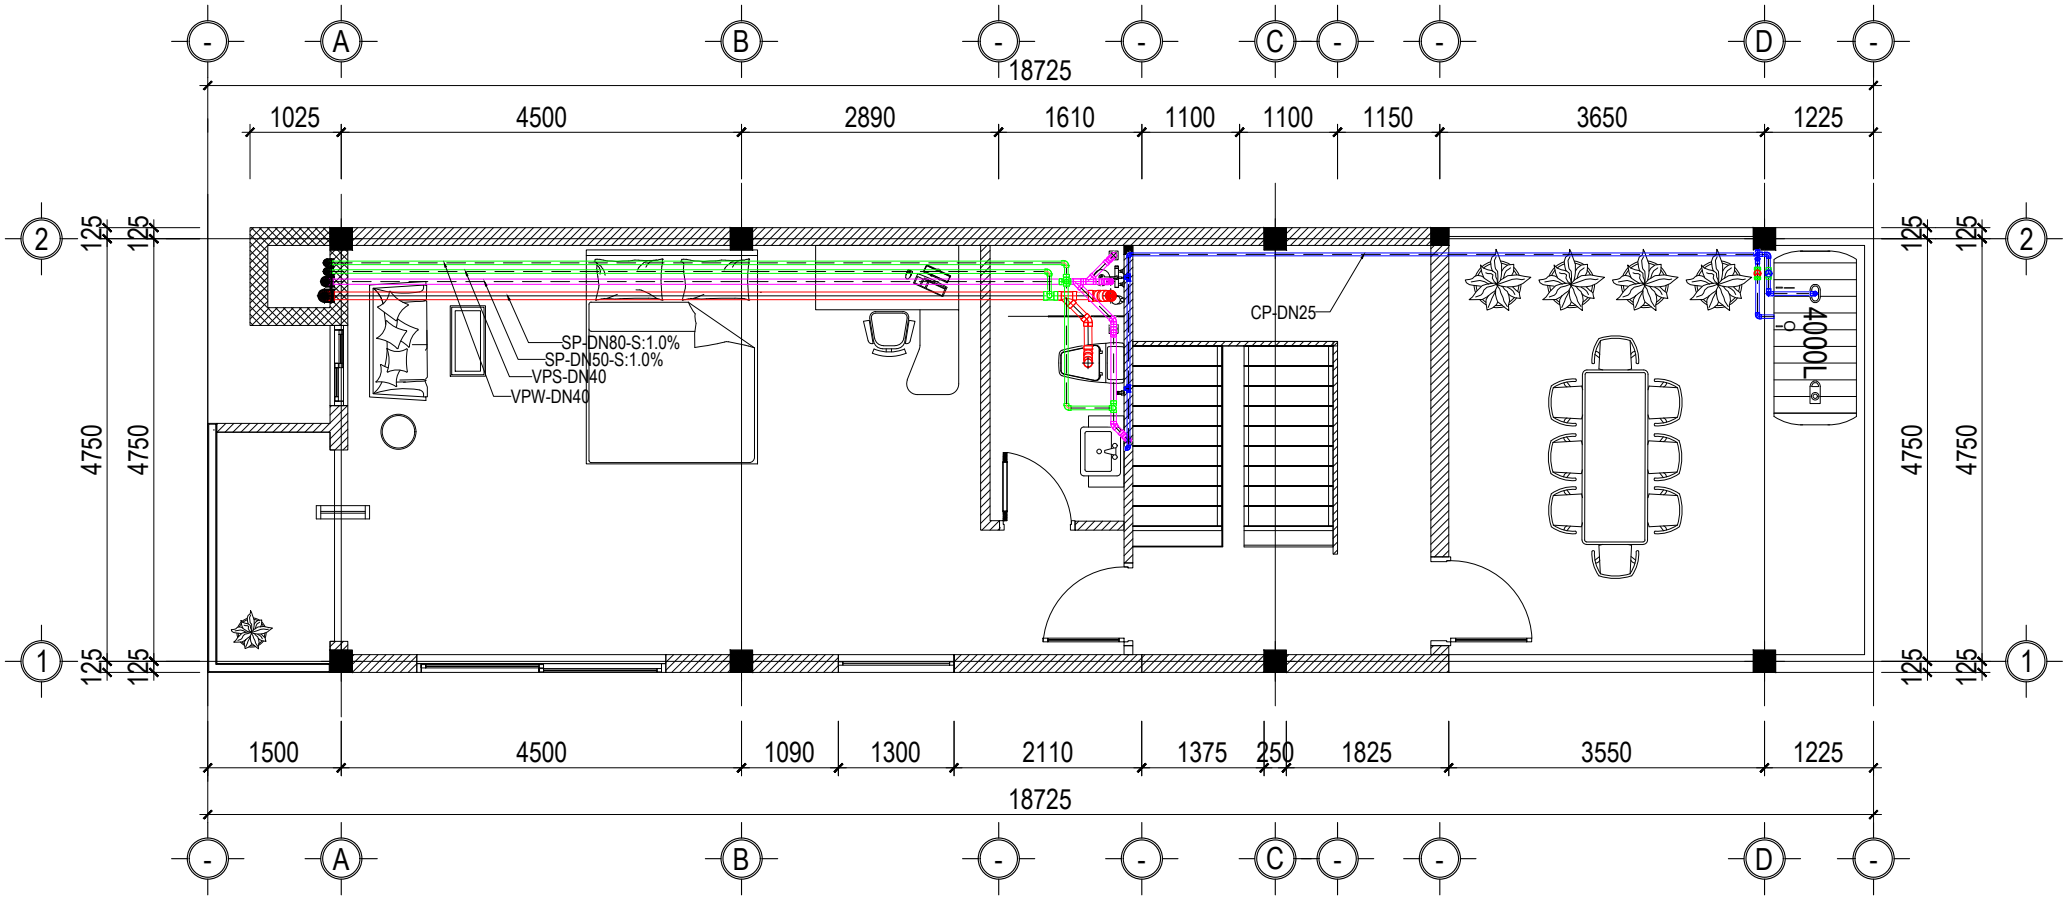

TERRACE FLOOR

SCALE : 1/85

GROUND FLOOR		
SP	3"	80mm
WP	2"	50mm
VSP	1.5"	40mm
VWP	1.5"	40mm
CP	1.5"	25mm

Course: Installation and Sanatary Lecturer: MAY Raksmey	Student: CHUCH Manet ID: e20220847	Plumbing Plan

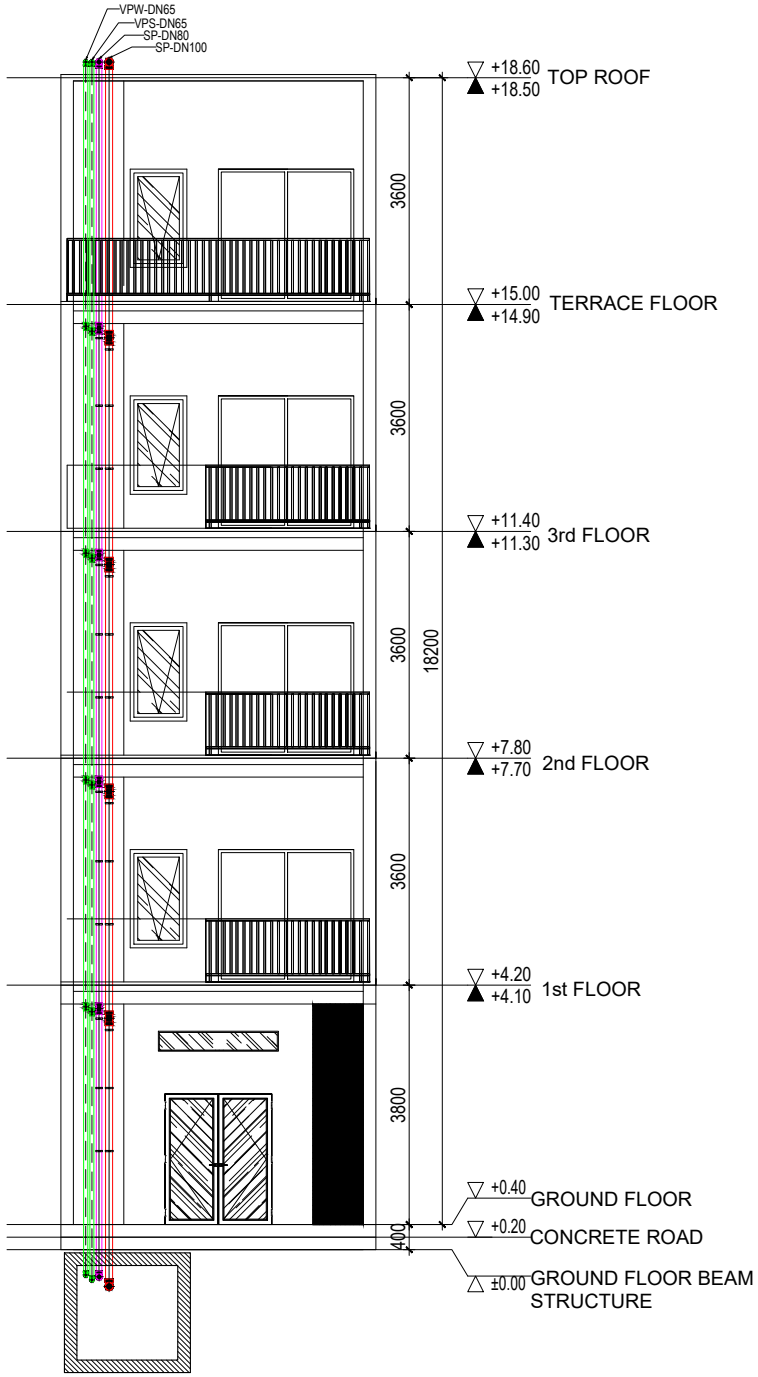

Course: Installation and Sanatary Lecturer: MAY Raksmey	Student: CHUCH Manet ID: e20220847	Plumbing Plan